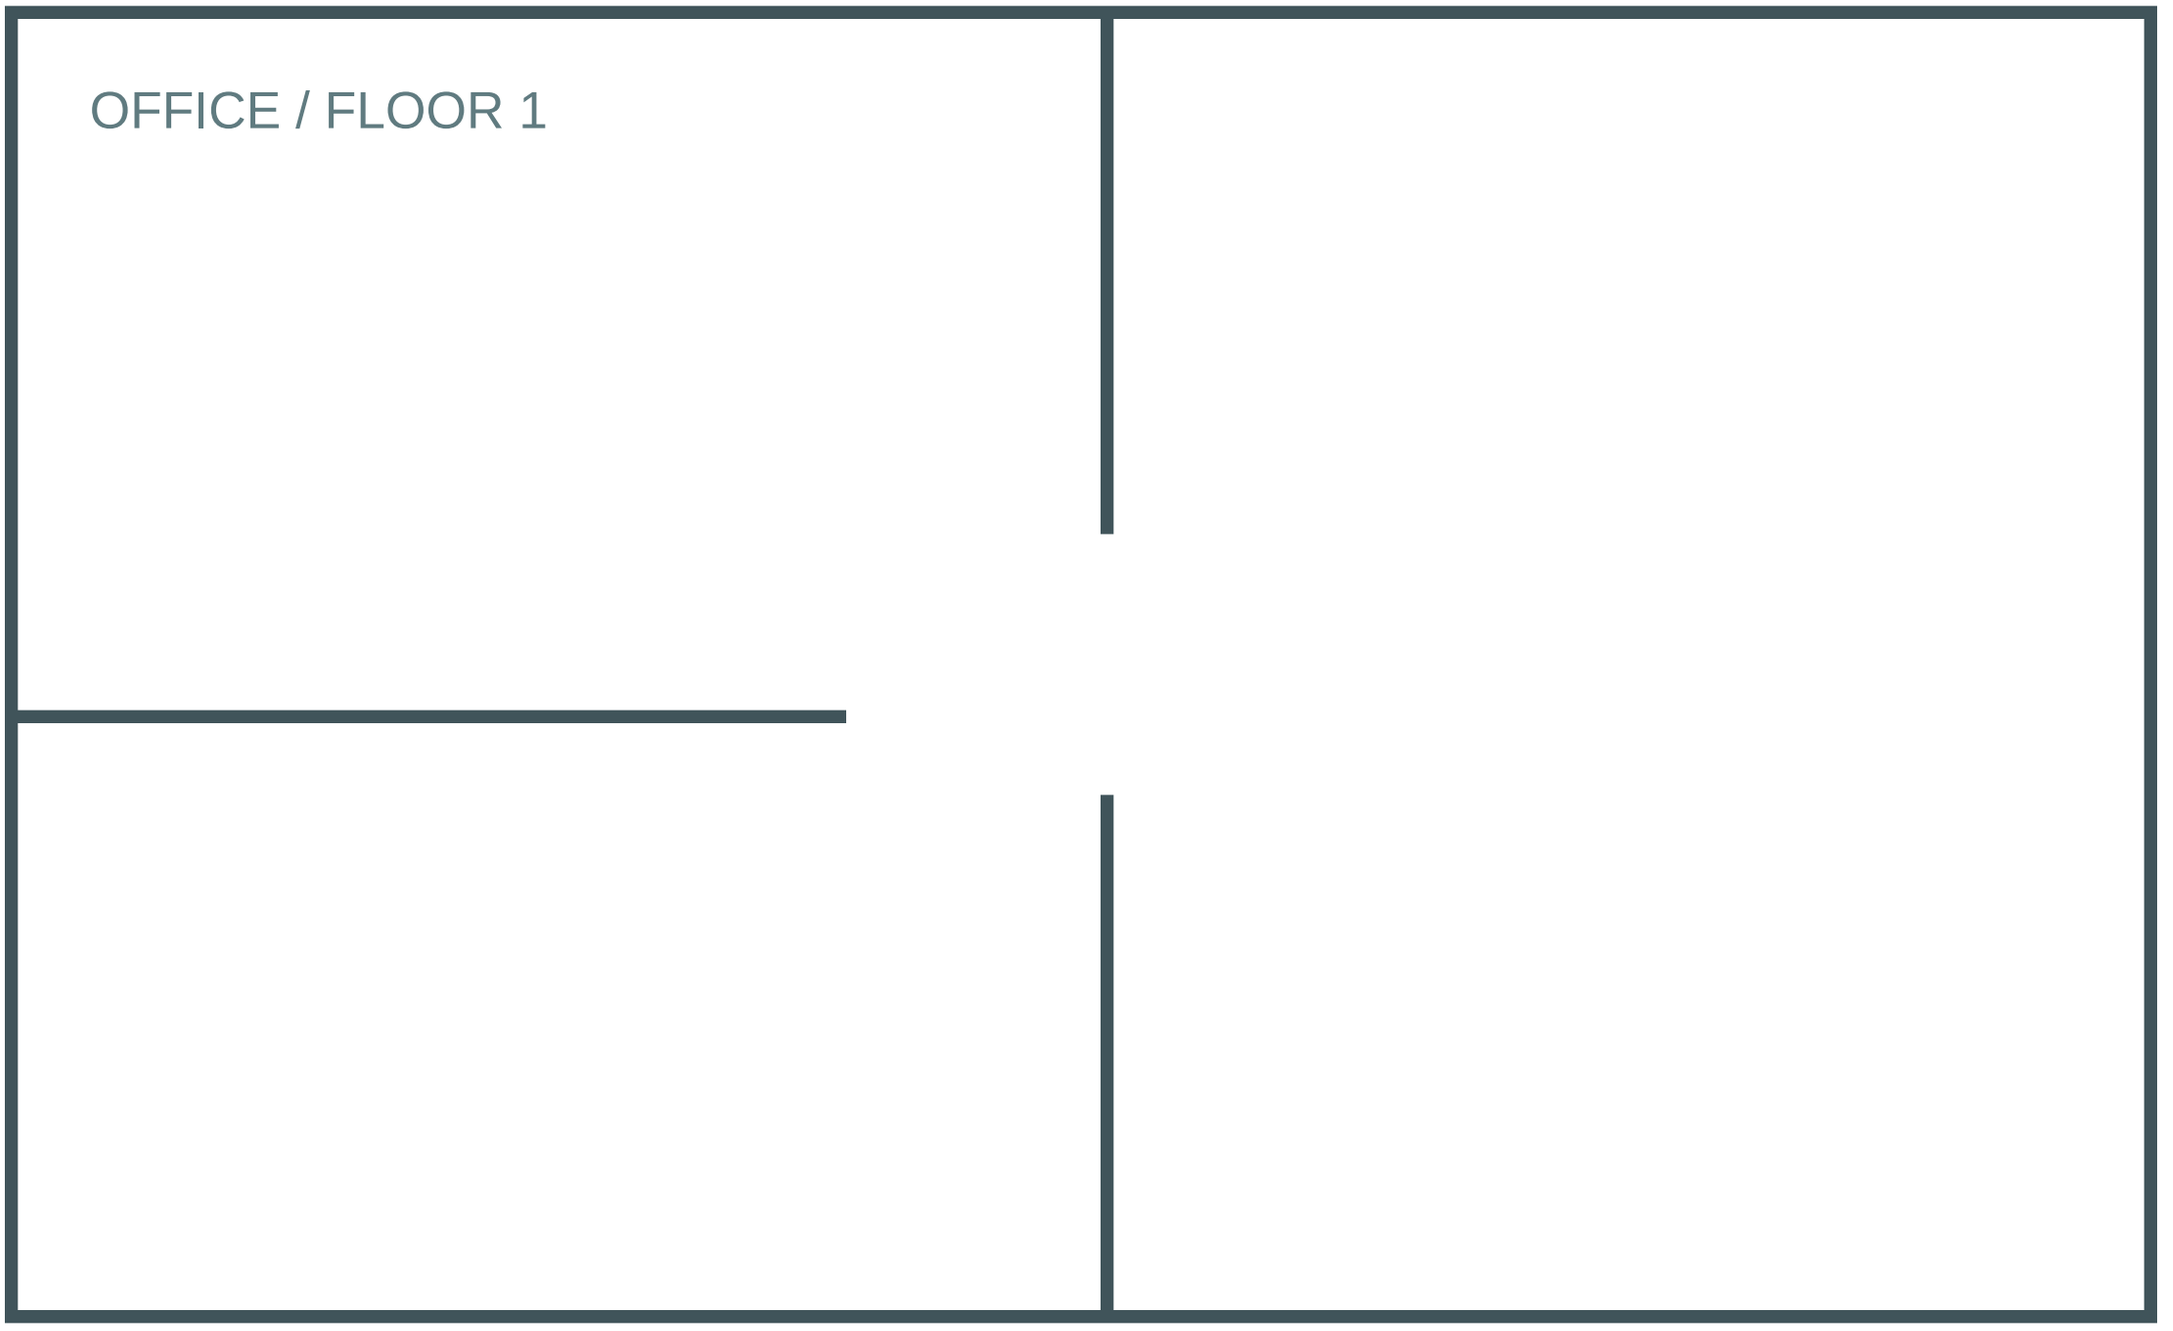
OFFICE / FLOOR 1

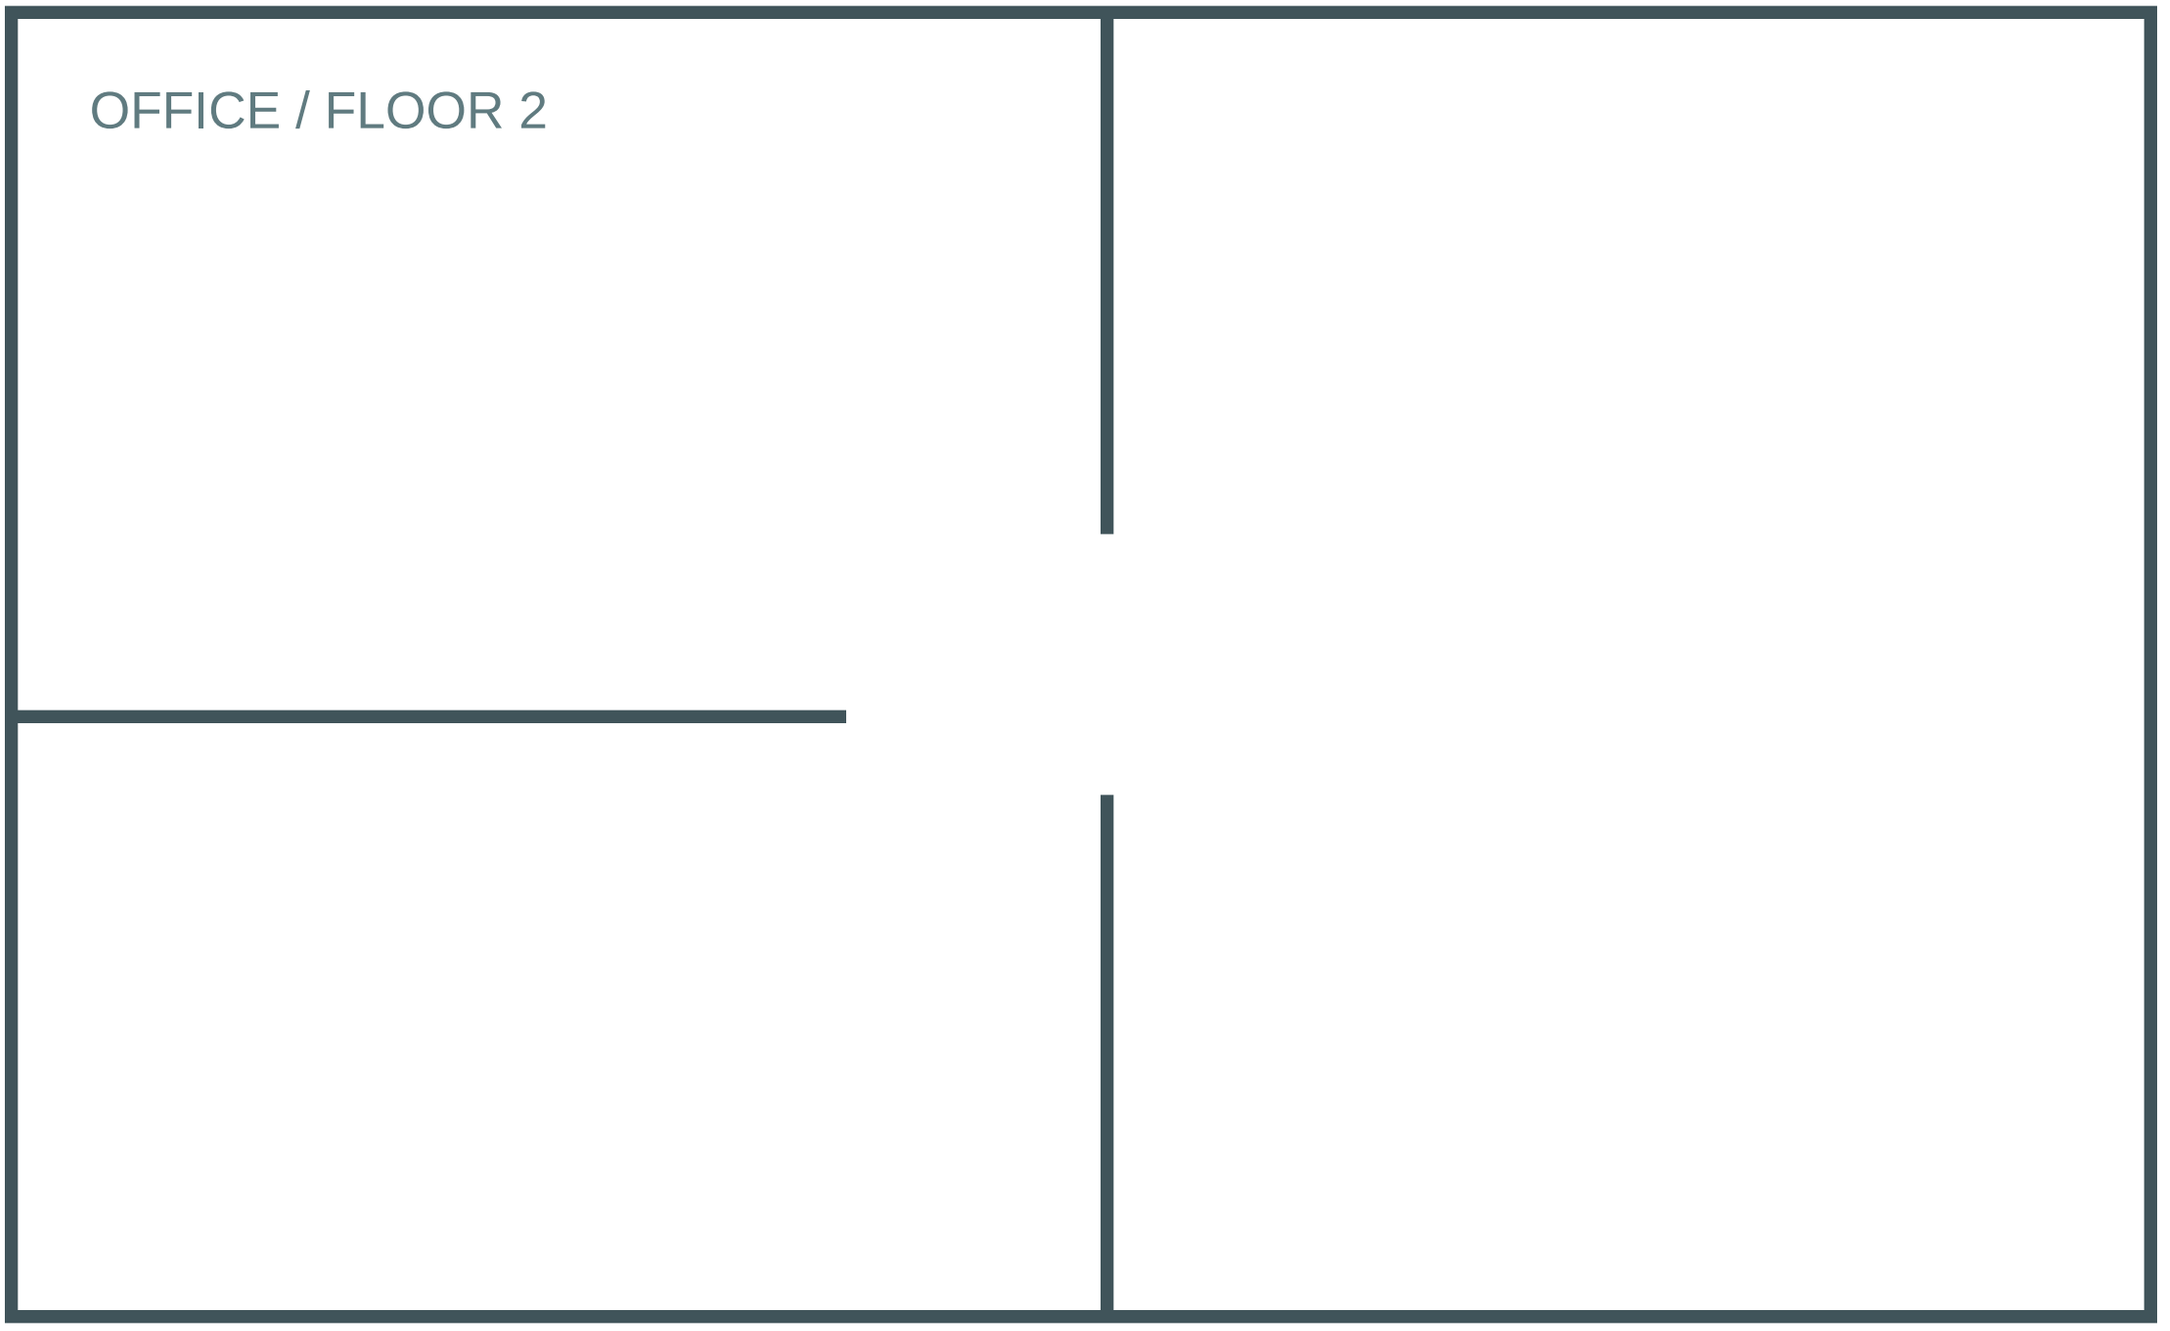
OFFICE / FLOOR 2